
第一章 供货安装方案与技术措施

第二节 土石方工程施工

期 **60日历天**
总体工期目标
合同签订后完成全流程施工

缆 **3295m**
电缆敷设长度
ZC-YJV22-26/35kV-3×300mm²

缓 **1至2天**
弹性缓冲时间
各阶段工序提前预留

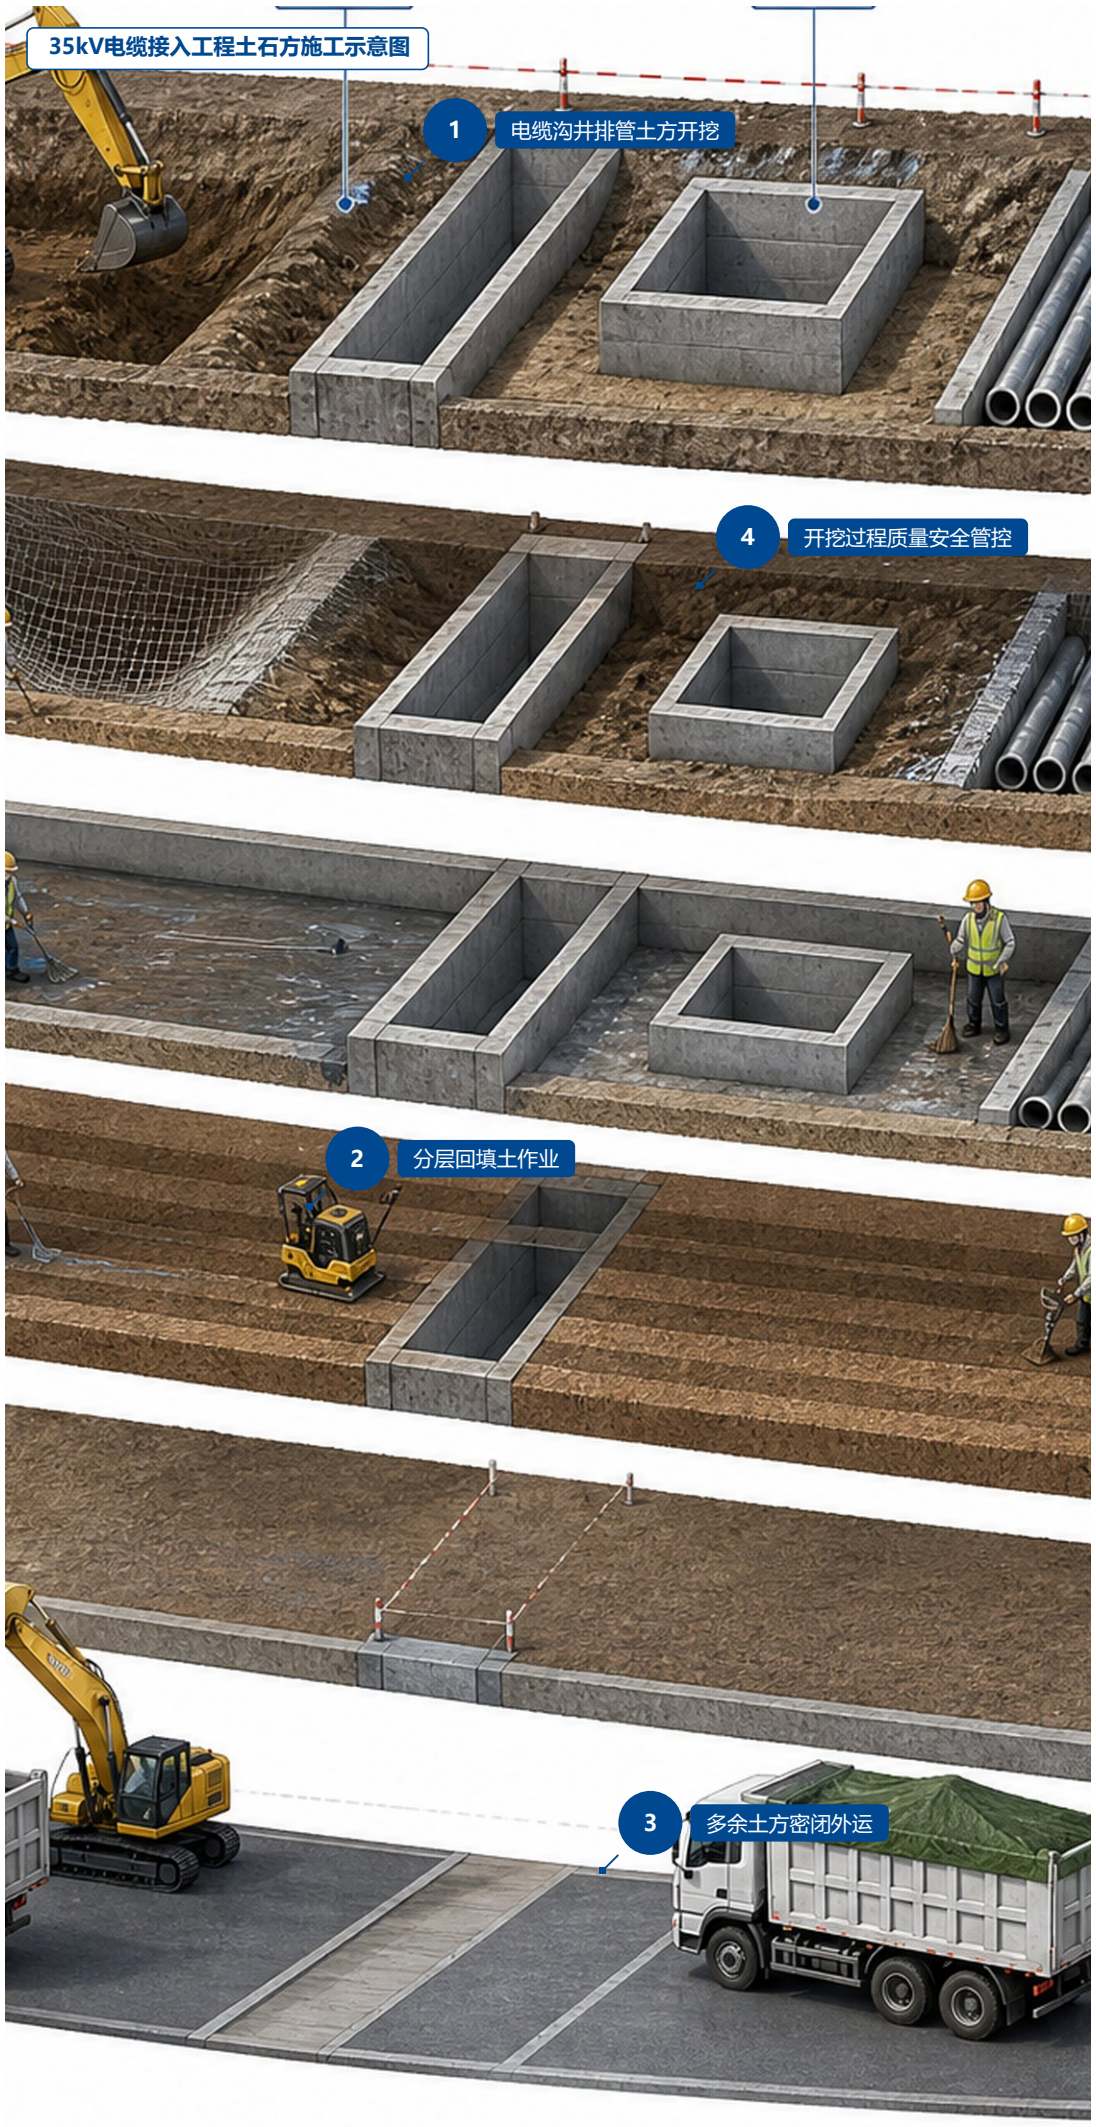

沿已完成测量放线定位的作业边界开展普通土开挖作业，控制开挖深度在2 至3 米区间 内，严格对齐电缆沟、工井、排管的设计作业面位置。选用斗容0.3m³ 的履带式挖掘机主导 开挖作业，开挖过程中预留150mm 厚的基底土层由人工清理找平，避免机械扰动基底原状土， 保证基底承载力符合设计要求。

开挖作业同步跟进坡面防护前置措施，作业面挖出一段即清理一段坡面浮土，为后续挂 网喷C25 混凝土60 厚的放坡支护工序预留充足作业空间，坡面坡度全程按规范要求控制， 随时排查边坡开裂、滑移风险。开挖产生的临时堆土沿沟槽边缘安全距离外有序堆放，避免 堆载过量挤压边坡造成垮塌隐患。

> 作业区域在行人车辆通行的出入口位置设置硬质隔离防护栏，悬挂明显的警示标牌，严禁无关人员随意进入开挖作业区域。

要 重点工序实施要点

	工序类别	主要工作内容及要点
①	施工准备	沿已完成测量放线定位的作业边界开展普通土开挖作业，控制开挖深度在2 至3 米区间内，严格对齐电缆沟、工井、排管的设计作业面位置。
②	土方与支护	开挖作业同步跟进坡面防护前置措施，作业面挖出一段即清理一段坡面浮土，为后续挂网喷C25 混凝土60 厚的放坡支护工序预留充足作业空间
③	旧通道处理	针对部分紧邻老旧电缆沟的开挖区段，提前探明地下既有管线的走向与埋深，采取人工探挖方式确认管线位置后再开展机械开挖，防止挖损既有运行管线。